


CORTES CIMIENTOS

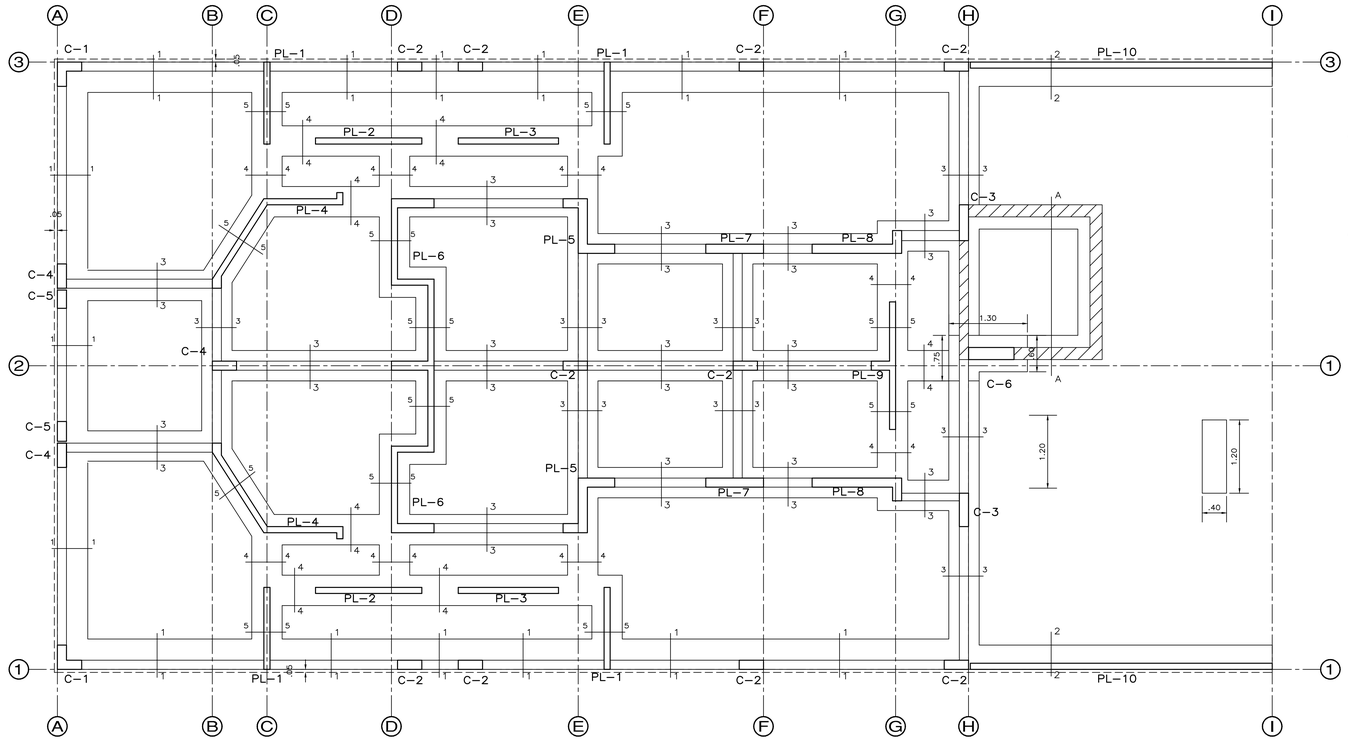


C I M E N T A C I O N

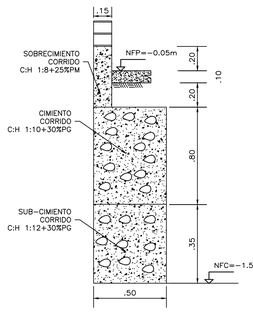


CORTE 1-1
ESC: 1/25

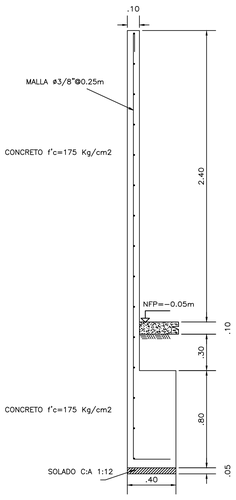


CORTE 2-2
ESC: 1/25

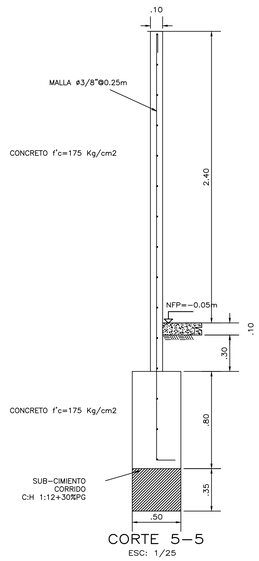


CORTE 5-5
ESC: 1/25

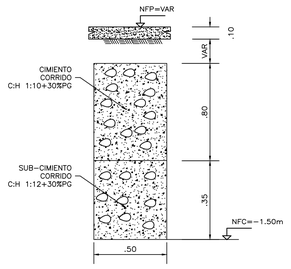

CORTE 4-4
ESC: 1/25

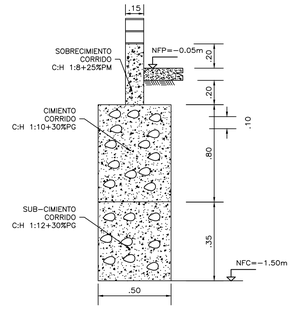

CORTE 3-3
ESC: 1/25

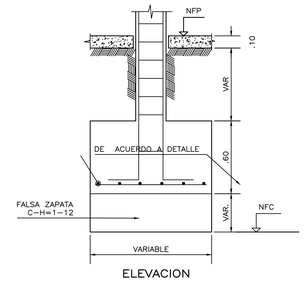


ELEVACION

DETALLE ZAPATA TIPICA

ESCALA: 1/25

CUADRO DE COLUMNAS

C-1 (Detalle)

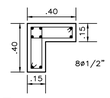

8ø1/2"

S ø1/4",1a .05,4 @.10
Rto @.25 a c/EXTR.

C-2 (0.15x0.40)



6ø1/2"

S ø1/4",1a .05,4 @.10
Rto @.25 a c/EXTR.

C-3(0.15x0.60)



8ø1/2"

S ø3/8",1a .05,4 @.10
Rto @.25 a c/EXTR.

C-4 (0.15x0.40)



6ø1/2"

S ø3/8",1a .05,4 @.10
Rto @.25 a c/EXTR.


C-5(0.15x0.30)



4ø1/2"

S ø1/4",1a .05,4 @.10
Rto @.25 a c/EXTR.

C-6(0.15x0.75)

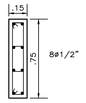

8ø1/2"

S ø3/8",1a .05,4 @.10
Rto @.25 a c/EXTR.

CUADRO DE PLACAS

PLACA	VERTICAL	HORIZONTAL	ESQUINAS
PL-1	ø8mm@0.20m	ø8mm@0.20m	1ø1/2"
PL-2	ø8mm@0.20m	ø8mm@0.20m	1ø1/2"
PL-3	ø8mm@0.20m	ø8mm@0.15m	1ø1/2"
PL-4	ø8mm@0.20m	ø8mm@0.20m	1ø1/2"
PL-5	ø8mm@0.20m	ø8mm@0.20m	1ø1/2"
PL-6	ø8mm@0.20m	ø8mm@0.15m	1ø1/2"
PL-7	ø8mm@0.20m	ø8mm@0.20m	1ø1/2"
PL-8	ø8mm@0.25m	ø8mm@0.20m	1ø1/2"
PL-9	ø8mm@0.20m	ø8mm@0.20m	1ø1/2"

ESPECIFICACIONES TECNICAS

ACERO	VARILLAS fy = 4,200 Kg/cm2.	
CONCRETO	f'c = 210 Kg/cm2.	
CONCRETO CICLOPEO	(CIMENTACION CORRIDA)	
SUB-CIMIENTO	C - H = 1:12+30% PIEDRA GRANDE 6" MAX.	
CIMIENTO	C - H = 1:10+30% PIEDRA GRANDE 6" MAX.	
SOBRECIMIENTO	C - H = 1:8 +25% PIEDRA MEDIANA DE 3" MAX.	
LADRILLO	TIPO KING-KONG A MAQUINA f'm = 35 Kg/cm2.	
MORTERO	CEMENTO - ARENA = 1:5 PARA ASENTADO DE LADRILLOS	
FALSO PISO	1:8 = CEMENTO HORMIGON	
TERRENO	PRESION ADMISIBLE σt = 4.00 Kg/cm2.	
RECUBRIMIENTOS	LOSAS ALIGERADAS Y MACIZAS	2.00 cm.
	VIGAS CHATAS	2.50 cm.
	MUROS, COLUMNAS Y VIGAS PERALTADAS	3.50 cm.
	ZAPATAS Y VIGAS DE CIMENTACION	7.50 cm.
SOBRECARGA	1er AL 4to PISO = 200 kg/m2	
	AZOTEA = 150 kg/m2	
TRASLAPES	ø3/8"= 40cm. ø3/4"= 70cm.	
	ø1/2"= 50cm.	
	ø5/8"= 60cm.	

NOTA:

- LLENAR EL CONCRETO DE LAS COLUMNAS ENTRE MUROS DENTADOS.
- LAS PAREDES INDICADAS EN LOS PLANOS DE ALIGERADOS SERAN DE LADRILLO KING-KONG, LAS PAREDES NO INDICADAS EN LOS PLANOS DE ALIGERADOS SERAN DE LADRILLO PANDERETA Y/O KING-KONG Y SE ELEVARAN A SU ALTURA FINAL DESPUES DEL DESENCOFRADO DEL ALIGERADO RESPECTIVO.
- SE RECOMIENDA TENER CUIDADO DE CONTROLAR EN LO POSIBLE CUALQUIER INFILTRACION DE AGUA QUE ALTERE EL EQUILIBRIO POTENCIAL DEL SUELO.
- LA ALTURA DE LOS SUB-CIMIENTOS SE COMPATIBILIZARA CON EL EMS,

PARAMETROS SISMICOS

Z=0.40; U=1.00; S=1.00 (Tp=0.40); Rx=6 y Ry=6
C=2.50 Cortante Basal Vx=0.166 Peso Vy=0.166Peso

DESPLAZAMIENTO MAXIMO DE ENTREPISO
deltaxx=11.741mm deltayy=13.464mm

RESUMEN : SUELOS

PRESION ADMISIBLE σt = 4.00 Kg/cm2.
PROFUNDIDAD DE CIMIENTOS: 1.50 m.
TIPO DE TERRENO: GRAVA ARENOSA (GP)
POBREMENTE GRADUADA

PROYECTO:
EDIFICIO MULTIFAMILIAR

PROPIETARIO
ALONSO BERNALES BELLEZA Y SRA

UBICACION:
CALLE RIO TAMBO 125 PUEBLO LIBRE

LAMINA N°:
E-01

PROFESIONAL:
Ing. CARLOS RIOS SANCHEZ
C.I.P. 60941

DIBUJO:	ESCALA:	FECHA:	PLANO:
CRS/REV002	1/50	ABRIL 2005	*CIMENTACION*