

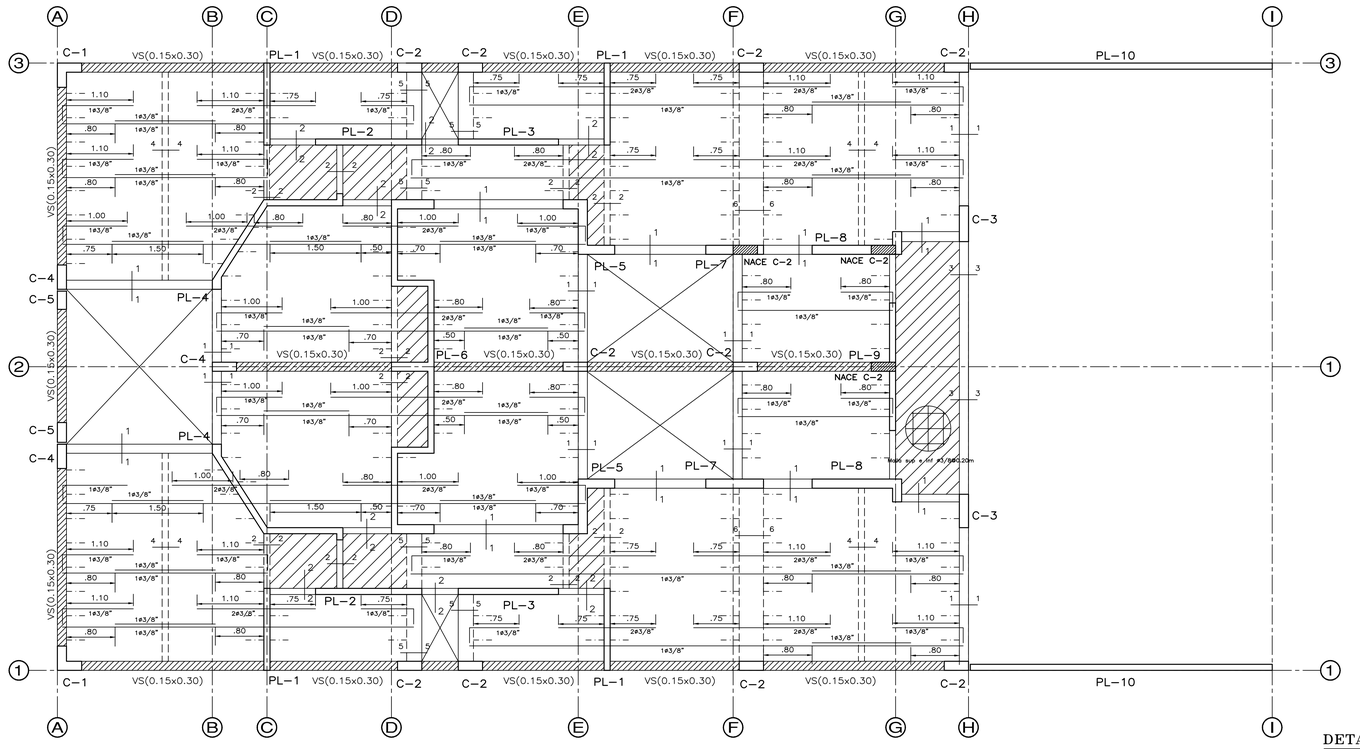



ALIGERADO 4TO NIVEL S/C: 150 Kg/m2 e=17cm

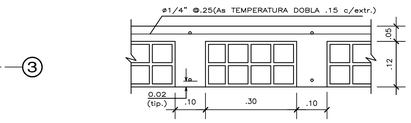

DETALLE: ALIGERADO TIPICO

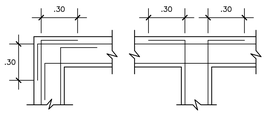

ENCUENTRO Y ANCLAJE
EN VIGAS CHATAS (PLANTA)

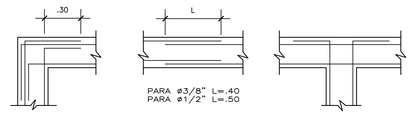

ENCUENTRO Y ANCLAJE EN VIGAS CHATAS (PLANTA)


ESCALA: 1/20

NOTA

a.- NO EMPALMAR MAS DE 50% DEL AREA TOTAL EN UNA MISMA SECCION

b.- EN CASO DE NO EMPALMAR EN LAS ZONAS INDICADAS O CON LOS PORCENTAJES ESPECIFICADOS AUMENTAR LA LONGITUD DE EMPALME EN UN 70%


c.- PARA ALIGERADOS Y VIGAS CHATAS, EL ACERO INFERIOR SE EMPALMARA SOBRE LOS APOYOS SIENDO LA LONGITUD DE EMPALME IGUAL A 25 cm. PARA FIERRO DE 3/8" Y 35cm. PARA ø 1/2" O ø 5/8"

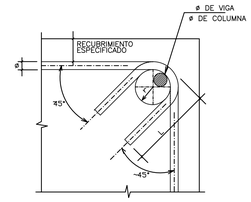


ø	r	L
1/4" ó 6 mm	2	10
3/8" ó 8 mm	3	15

DETALLE DE DOBLADO DE ESTRIBOS

ø	T m.	L1 m.	L2 m.
3/8"	.40	.45	.40
1/2"	.50	.50	.45
5/8"	.60	.55	.40

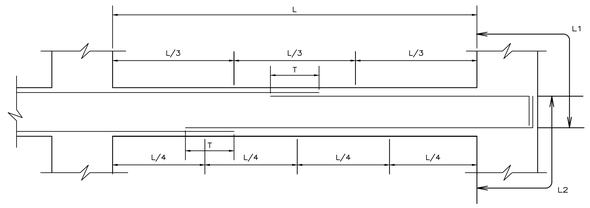


DETALLE DE ZONAS DE EMPALME EN VIGAS Y Llosas

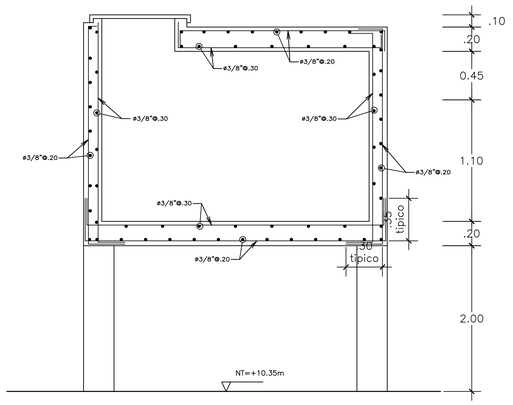


CORTE TANQUE ELEVADO

ESCALA 1/25

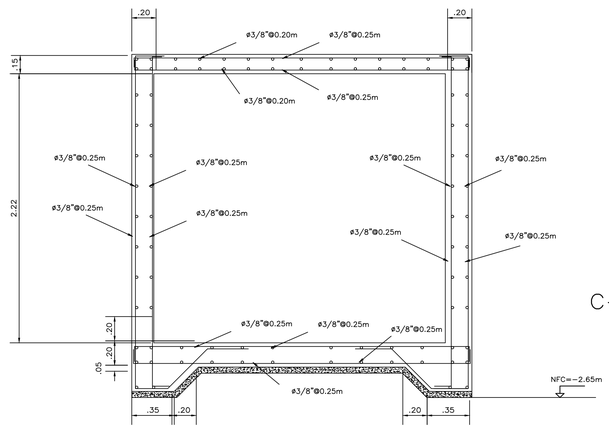


CORTE CISTERNA

ESC: 1/25

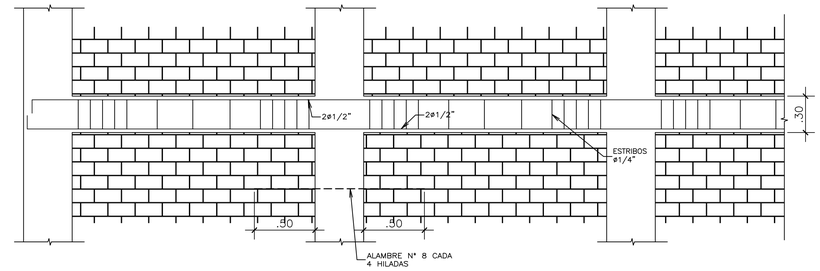

DETALLE. MURO PORTANTE TIPICO

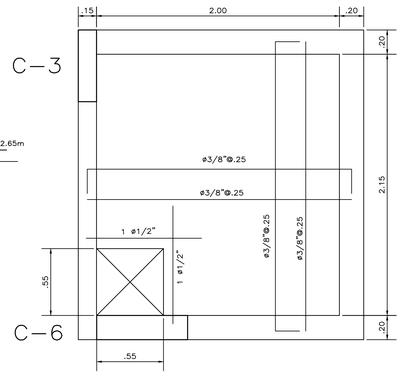

TECHO CISTERNA

ESCALA: 1/20

PROYECTO:	EDIFICIO MULTIFAMILIAR
PROPIETARIO	*ALONSO BERNALES BELLEZA Y SRA*
UBICACION:	CALLE RIO TAMBO 125 PUEBLO LIBRE
PROFESIONAL:	Ing. CARLOS RIOS SANCHEZ C.I.P. 60941
LAMINA N°:	E-03
DIBUJO: CRS/REV002	ESCALA: 1/50
FECHA: ABRIL 2005	PLANO: *ALIGERADO 4TO NIVEL*